APPROVED AS TO IMPACT ON STATE FACILITIES AND CONFORMANCE WITH APPLICABLE STATE STANDARDS AND PRACTICES AND THAT TECHNICAL OVERSIGHT WAS PERFORMED.

DATE SIGNED

LICENSE Exp DATE

REGISTRATION No.

CALTRANS DESIGN OVERSIGHT APPROVAL

CONSULTANT DESIGN MANAGER

STATE OF CALIFORNIA
DEPARTMENT OF TRANSPORTATION
PROJECT PLANS FOR CONSTRUCTION ON

Dist	COUNTY	ROUTE	POST MILES TOTAL PROJECT	SHEET No.	TOTAL SHEETS
#	#	#	#	#	#

LOCATION MAP
Caltrans

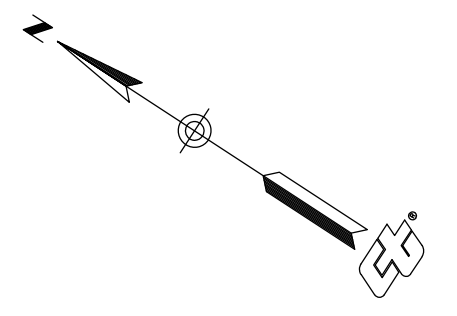

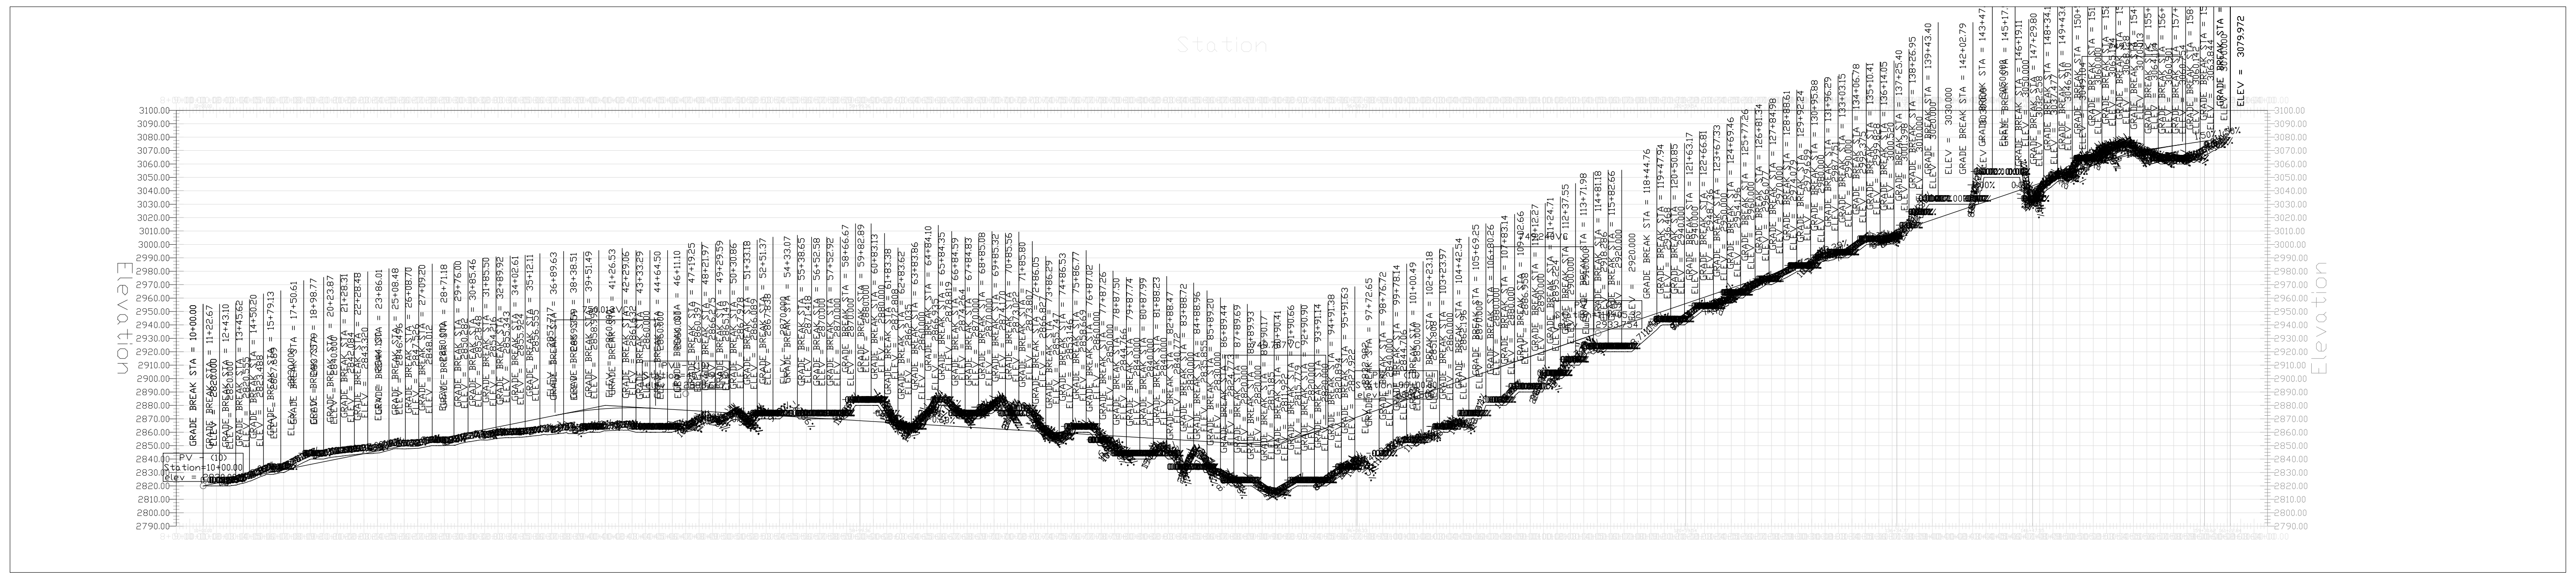

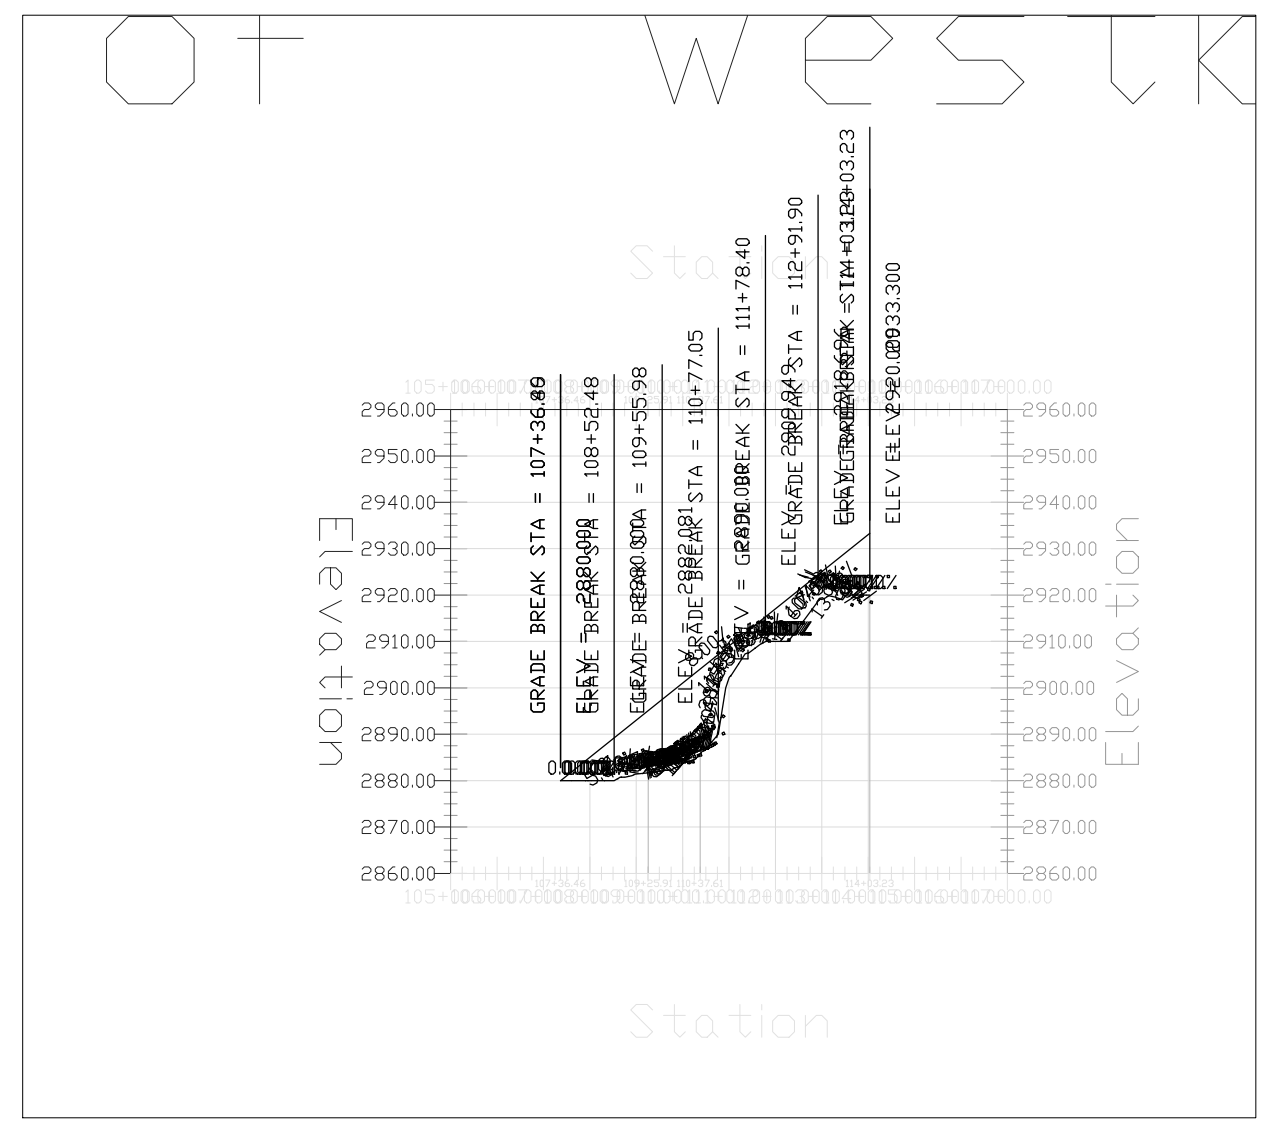

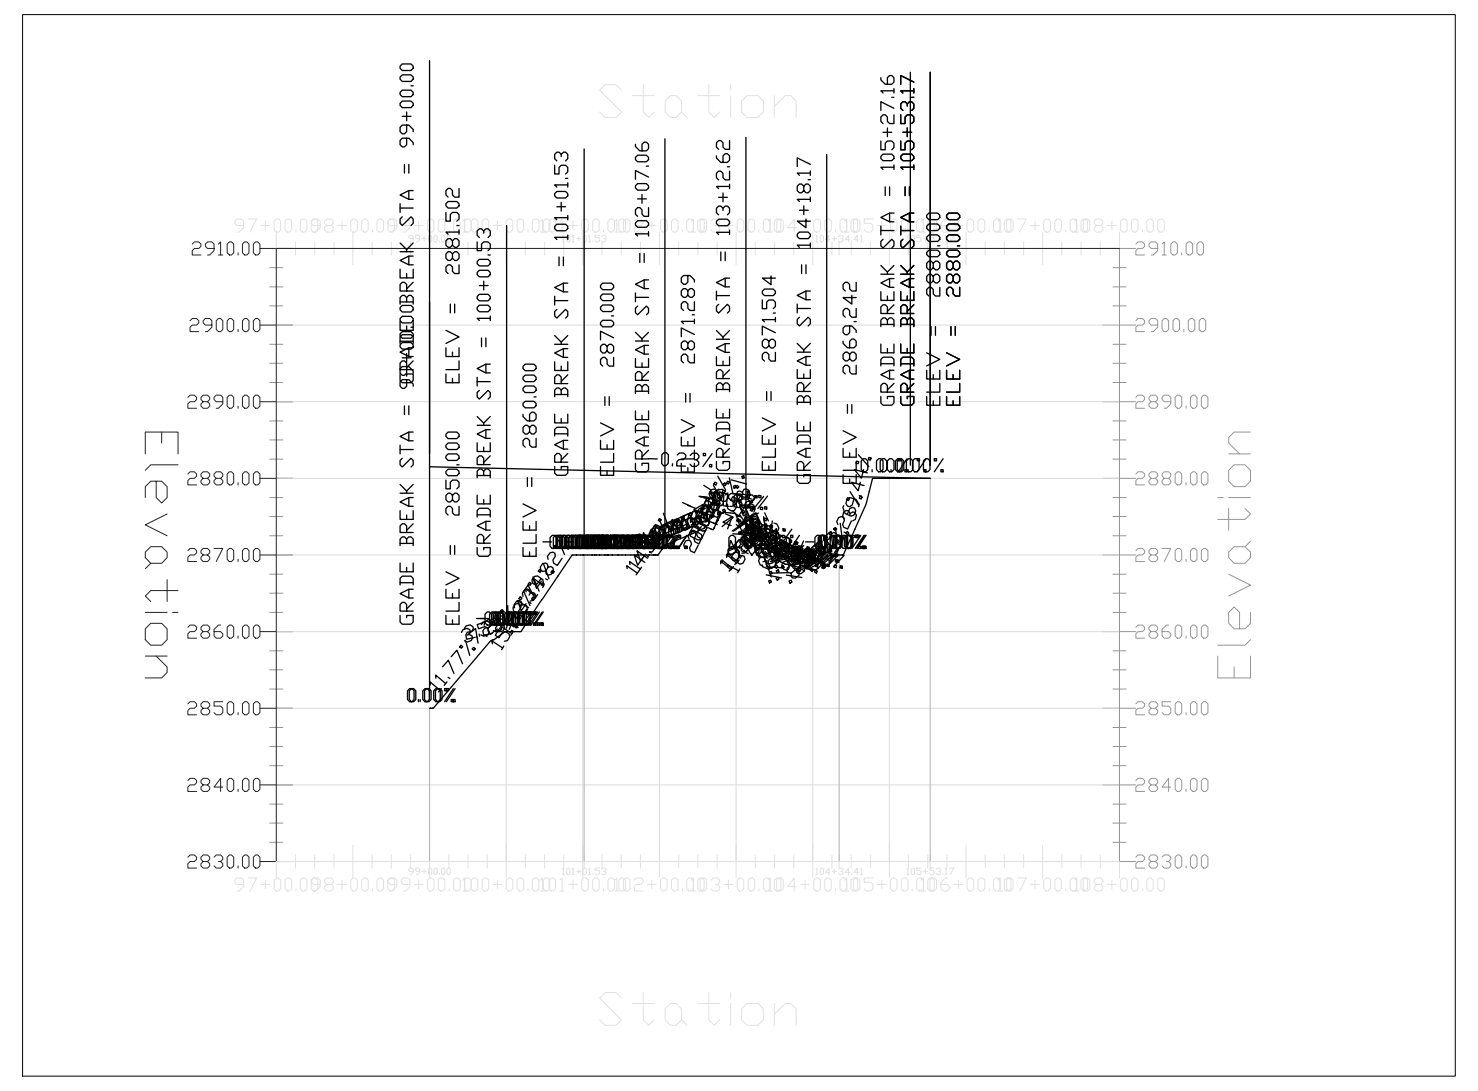

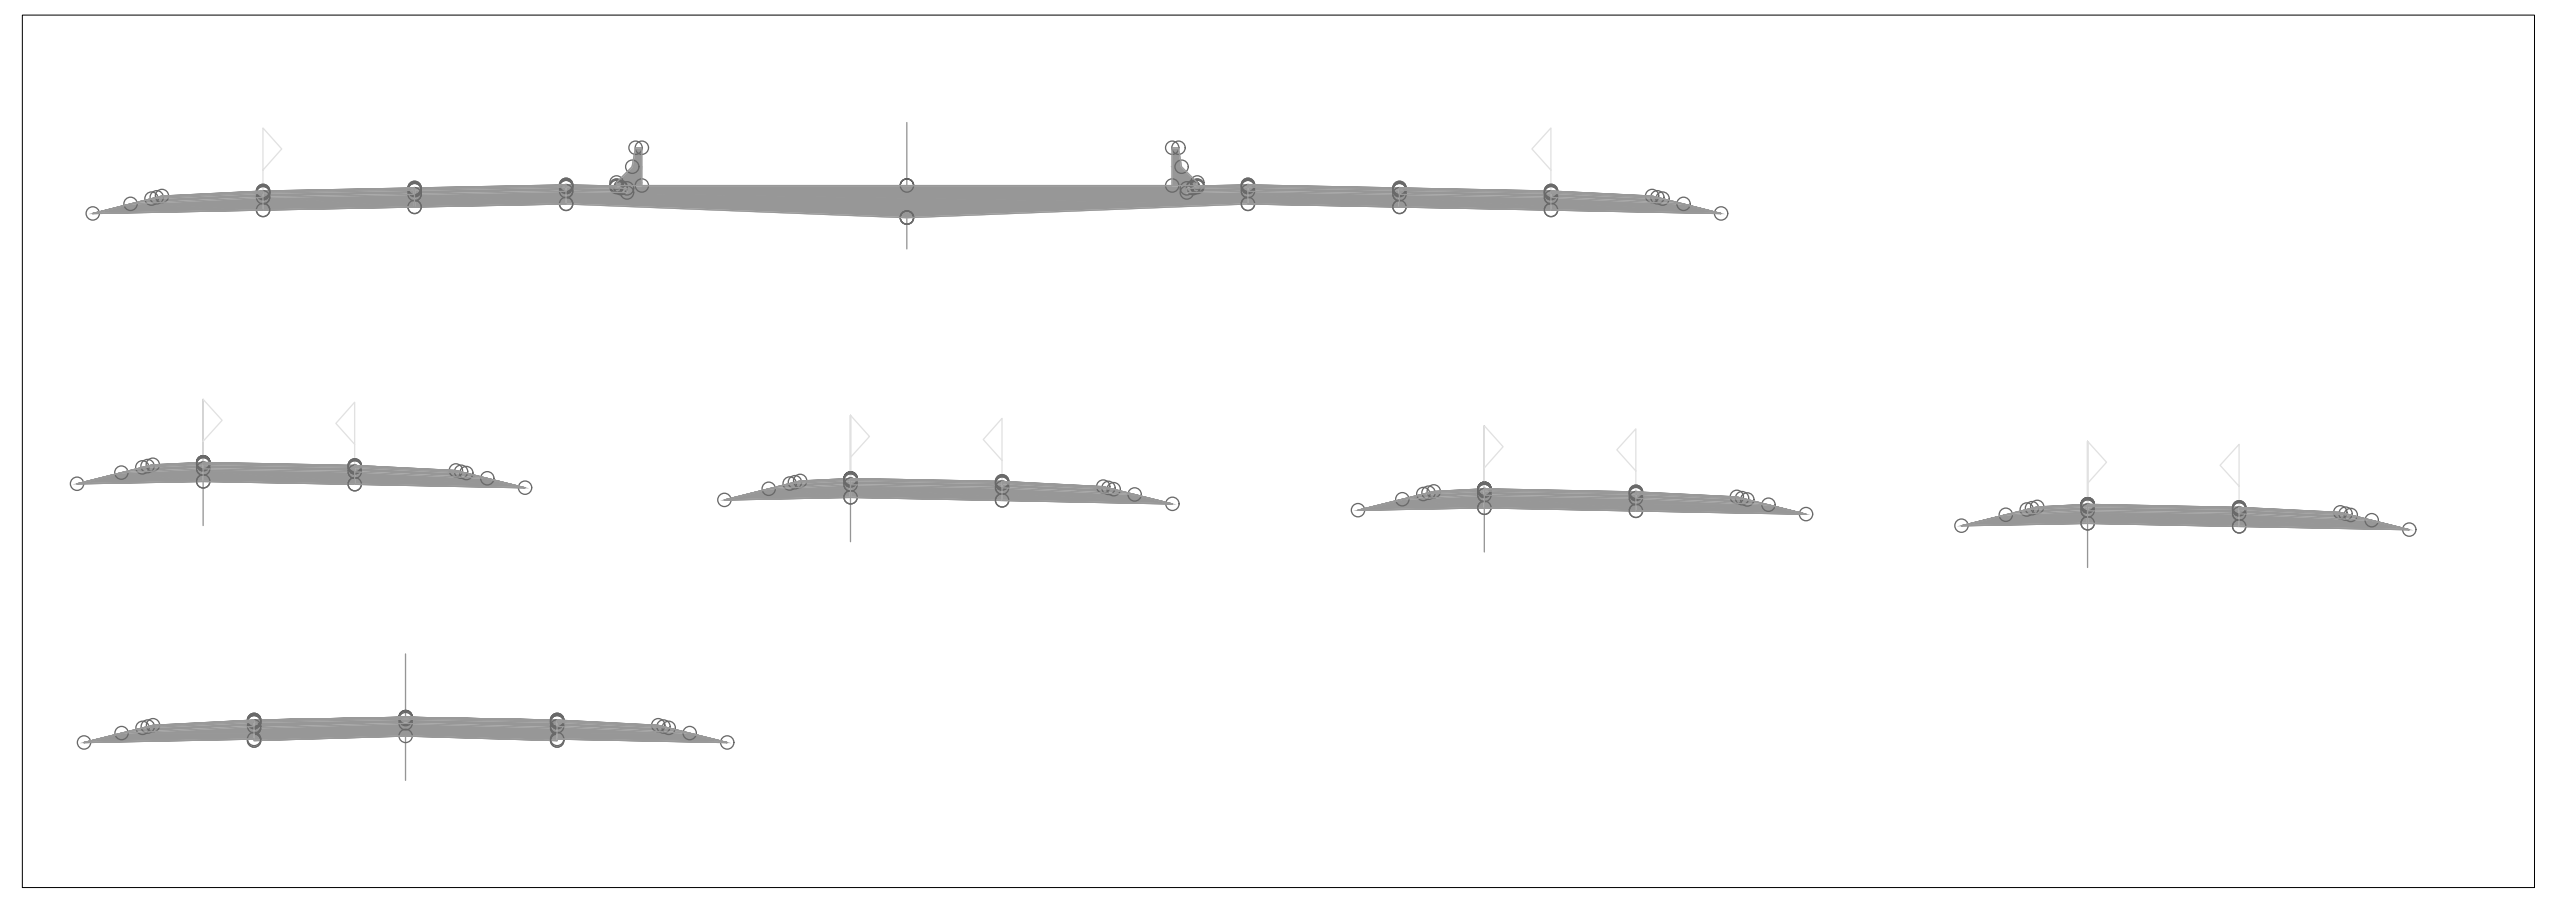

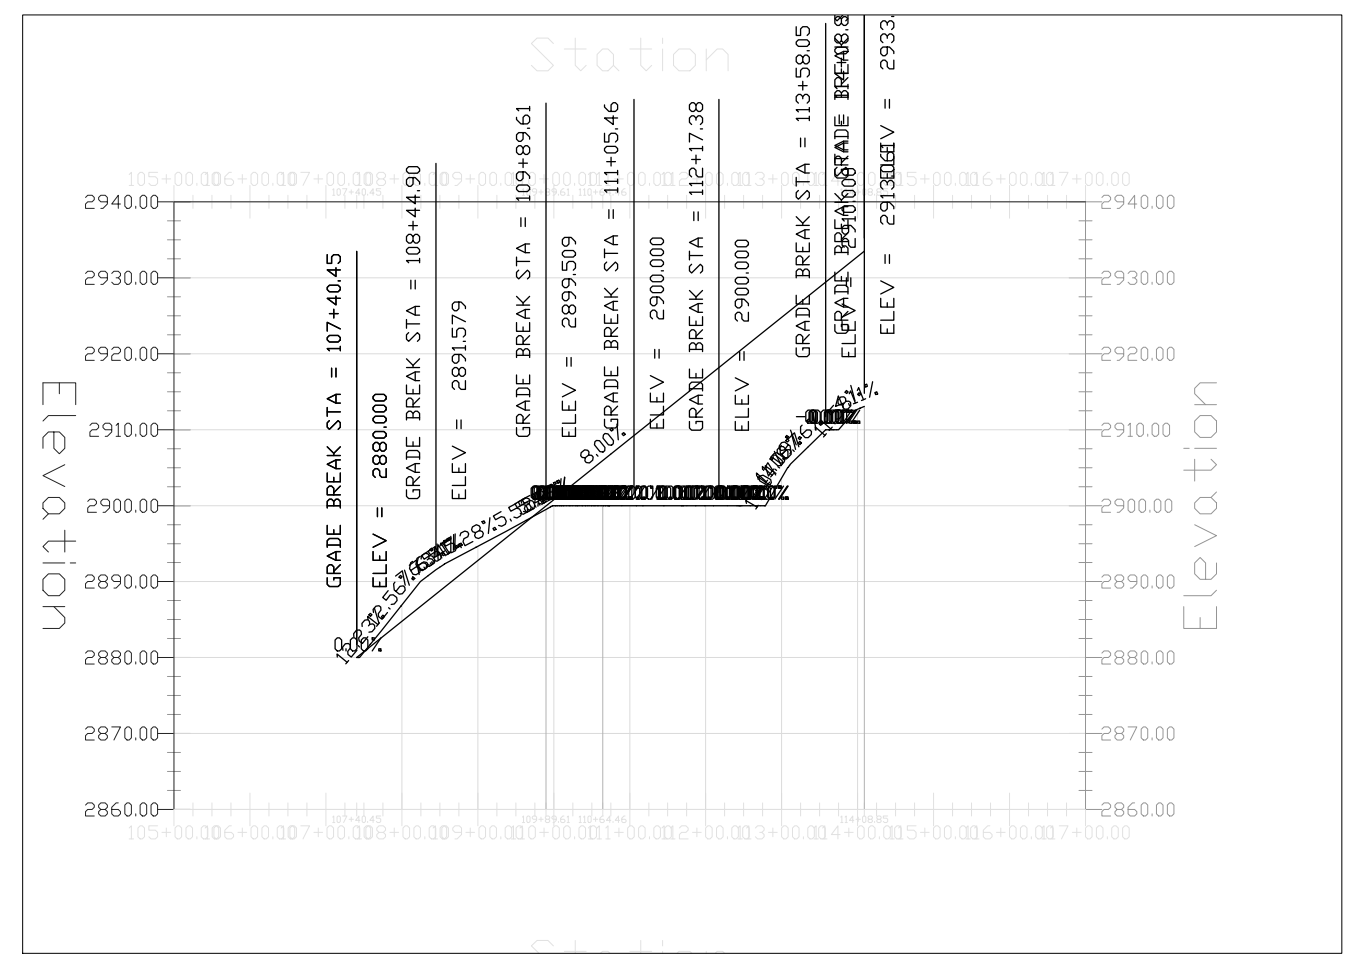

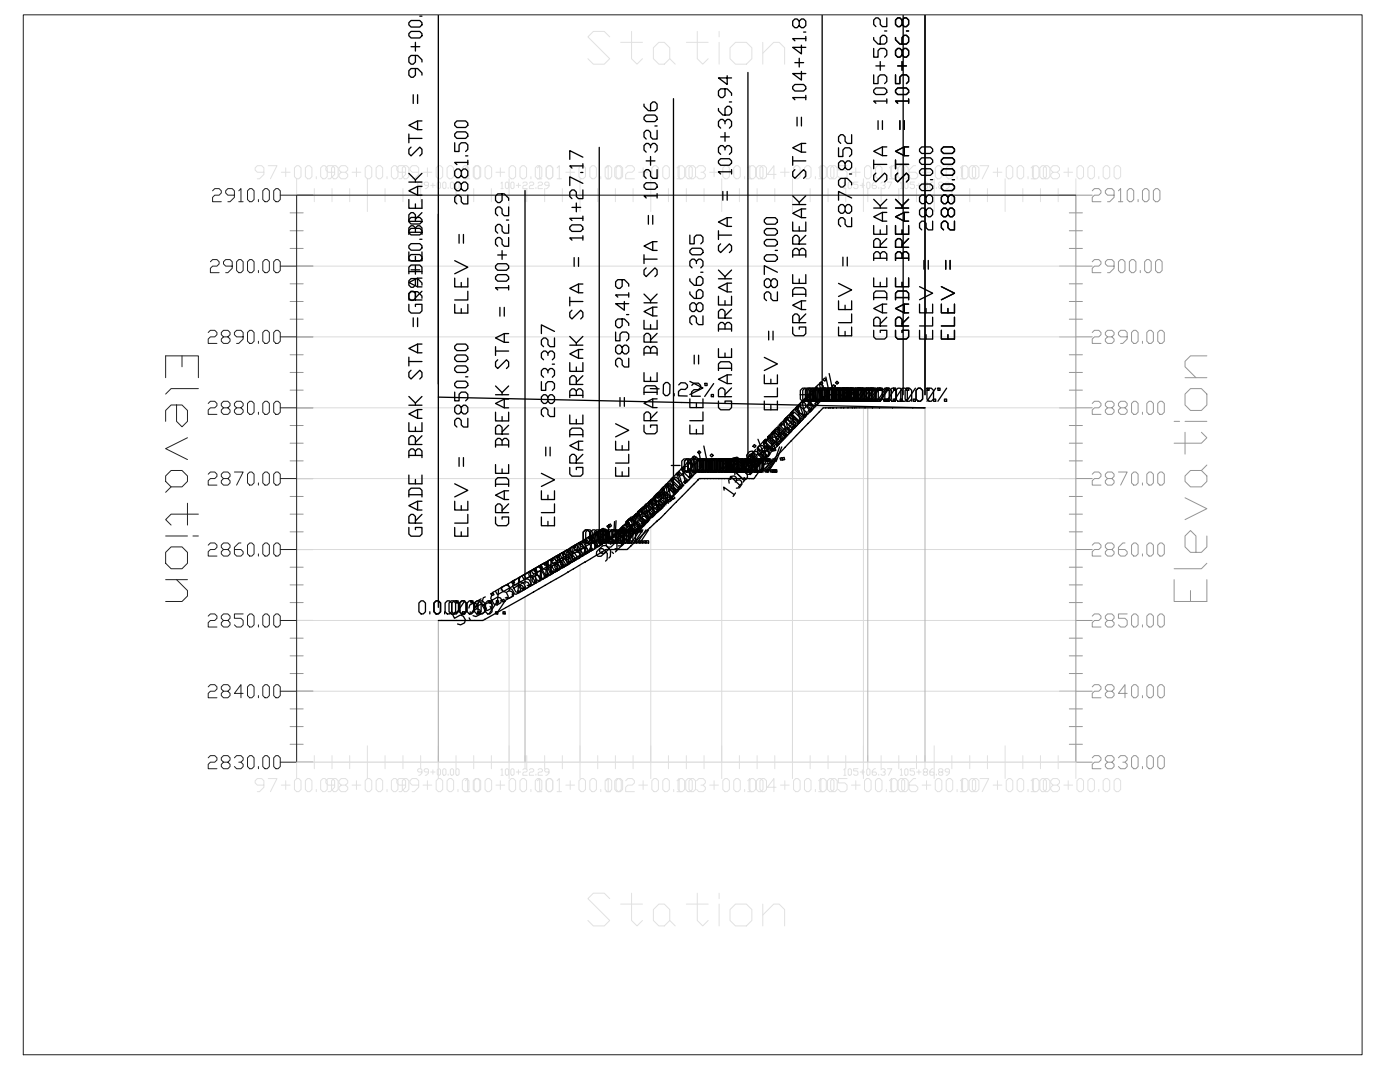

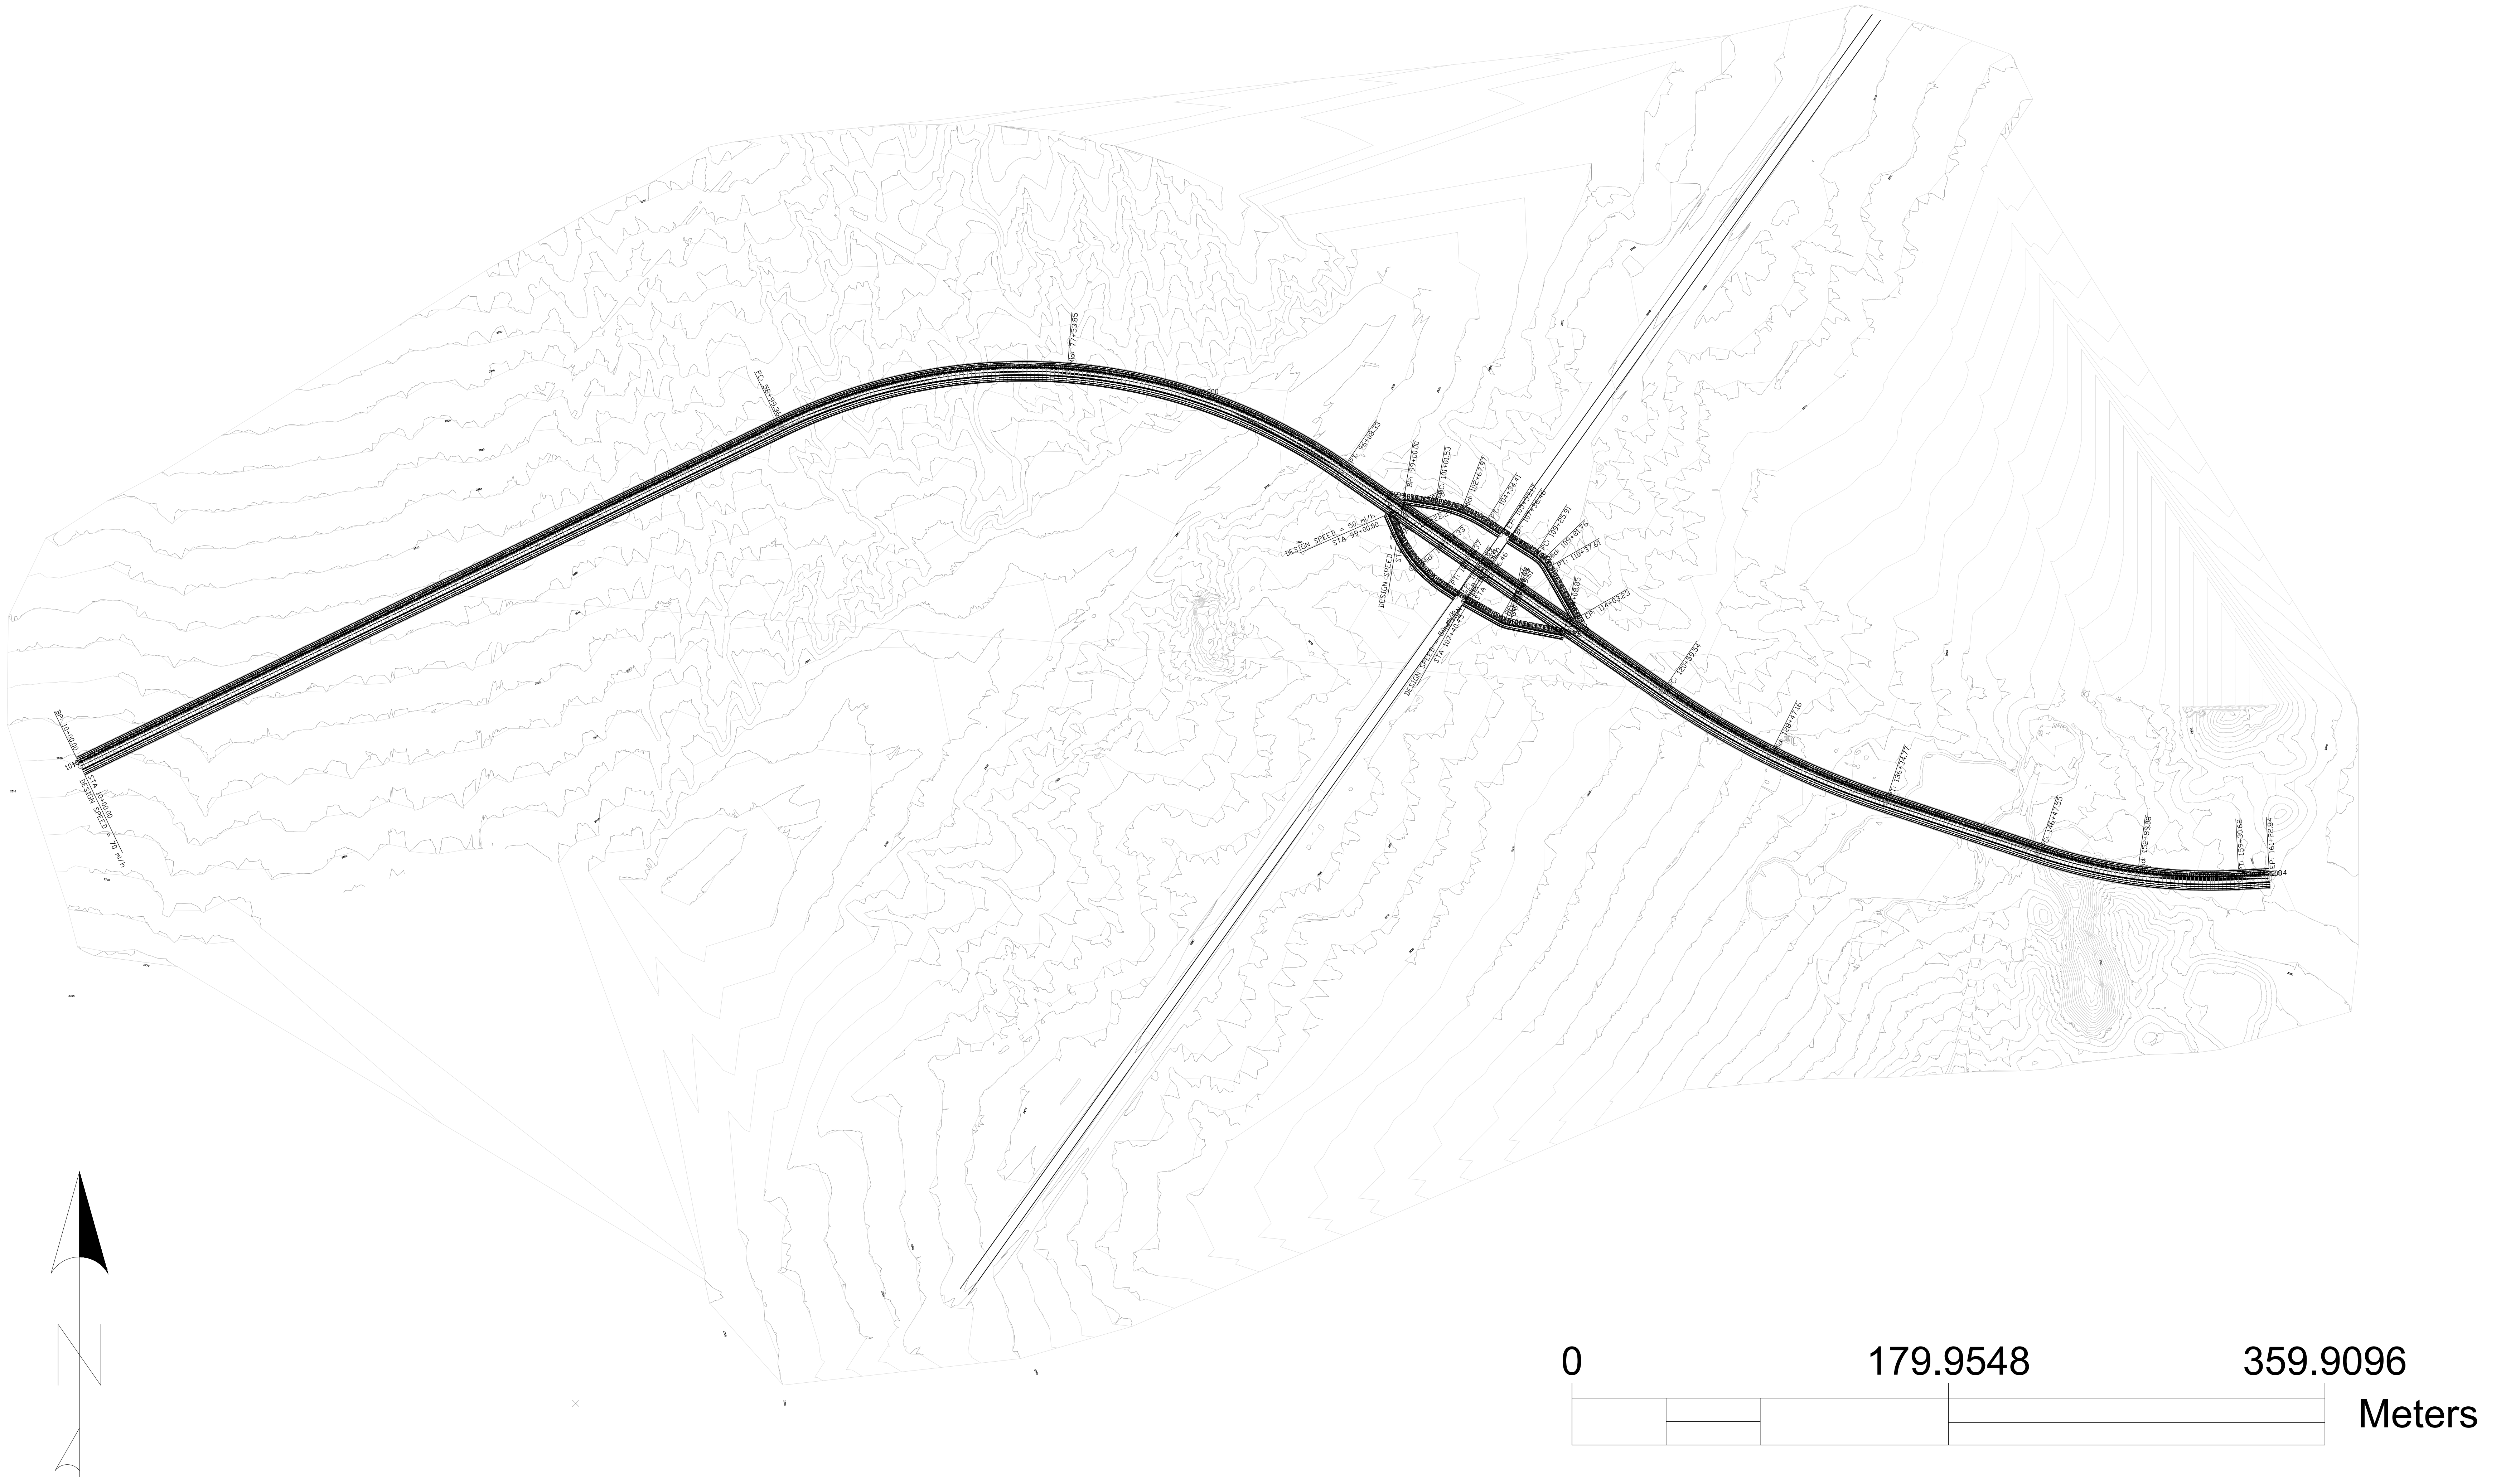

PROJECT ENGINEER DATE
REGISTERED CIVIL ENGINEER

REGISTERED PROFESSIONAL ENGINEER
No.
Exp.
STATE OF CALIFORNIA

PLANS APPROVAL DATE

THE STATE OF CALIFORNIA OR ITS OFFICERS OR AGENTS SHALL NOT BE RESPONSIBLE FOR THE ACCURACY OR COMPLETENESS OF SCANNED COPIES OF THIS PLAN SHEET.

GEOMETRIC APPROVAL DRAWING

CALIFORNIA STATE POLYTECHNIC
UNIVERSITY, POMONA.
TRANSPORTATION DESIGN PROJECT

AN ACADEMIC PARTNERSHIP WITH CALTRANS

PROJECT MANAGER	PROJECT ENGINEERS					

DATE PLOTTED =>
TIME PLOTTED =>
LAST REVISION 00-00-00

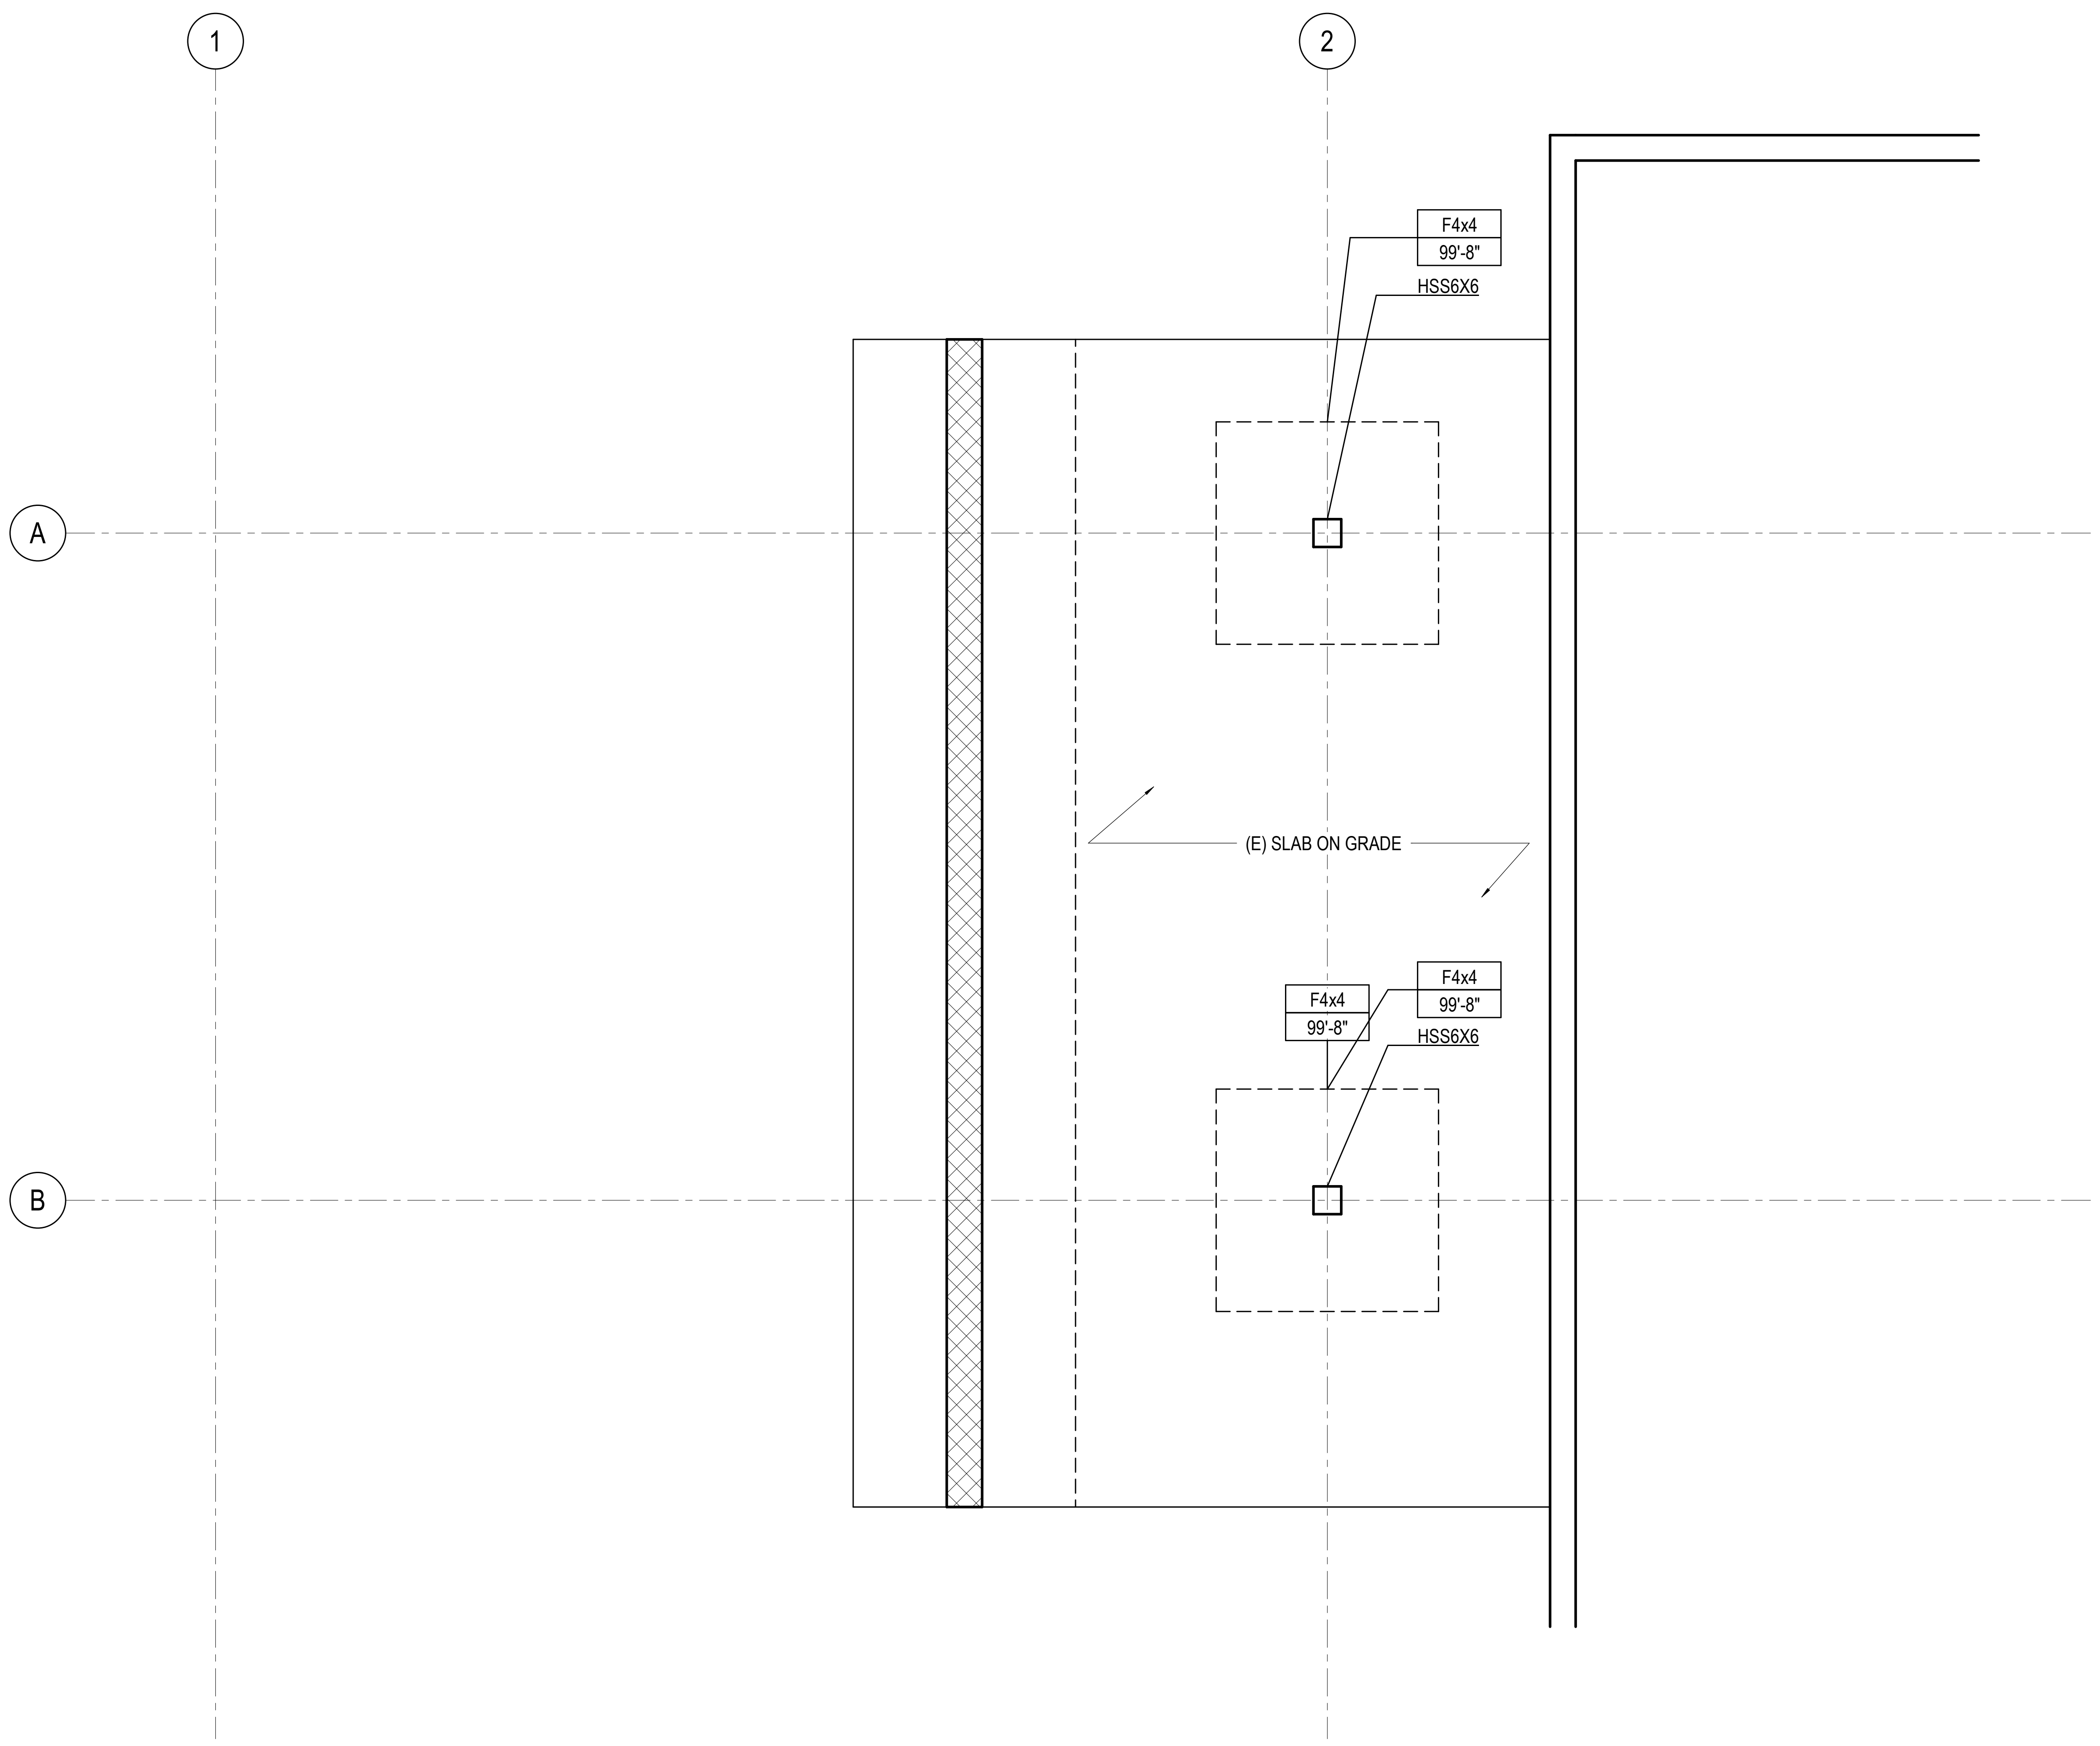

1 **LEVEL 1**
1/2" = 1'-0"

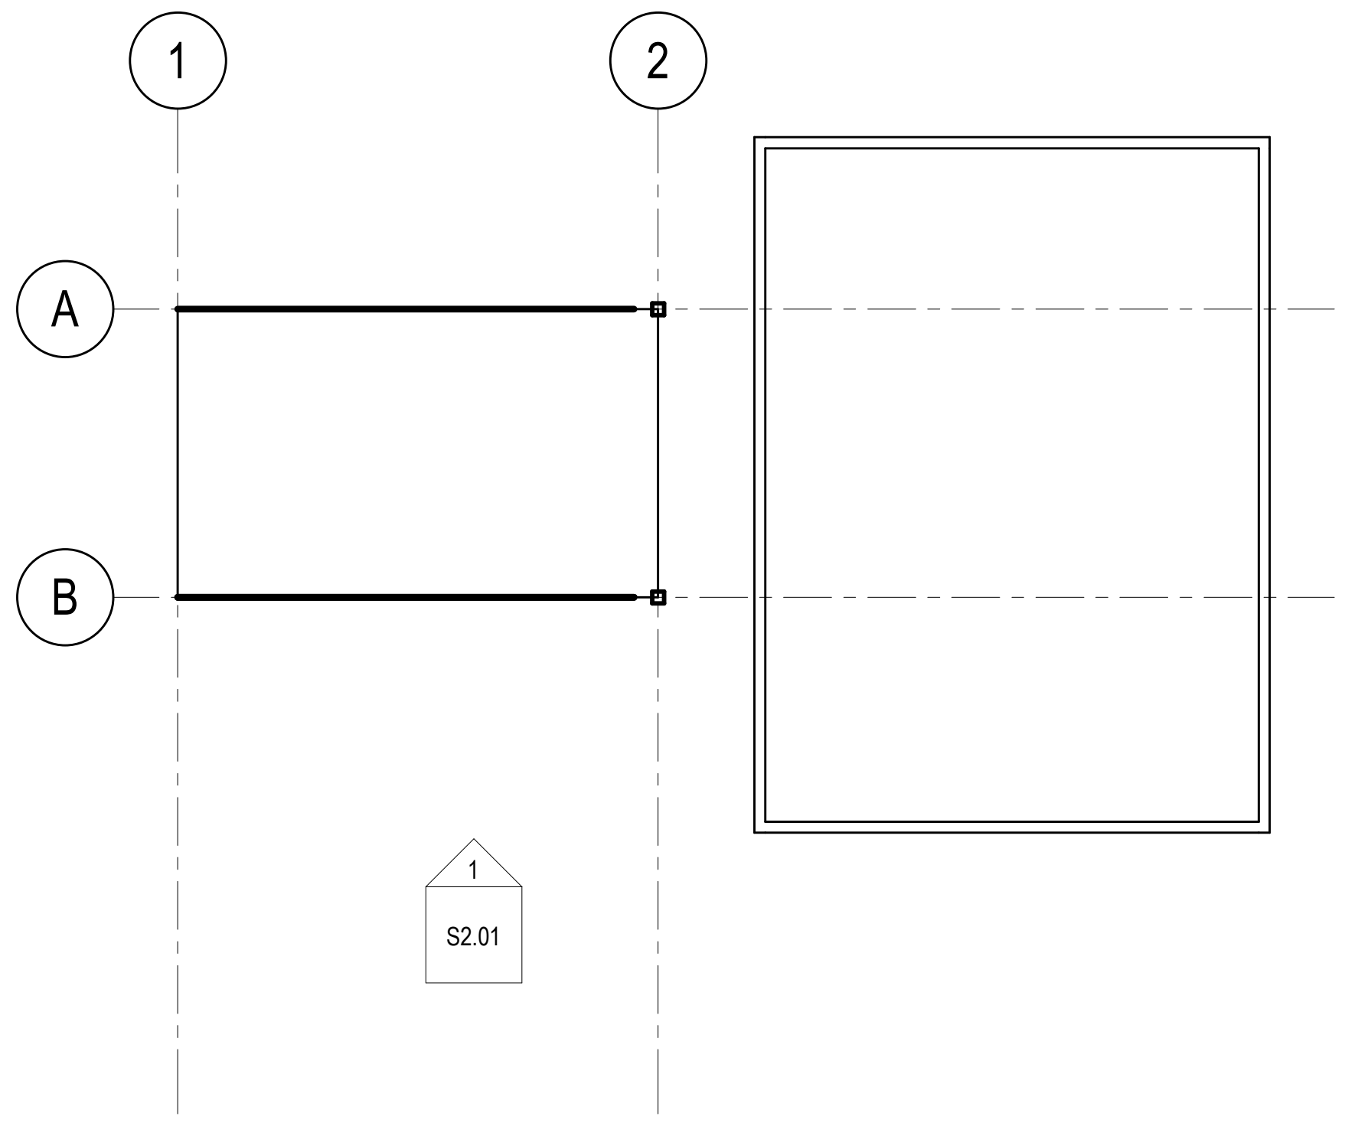

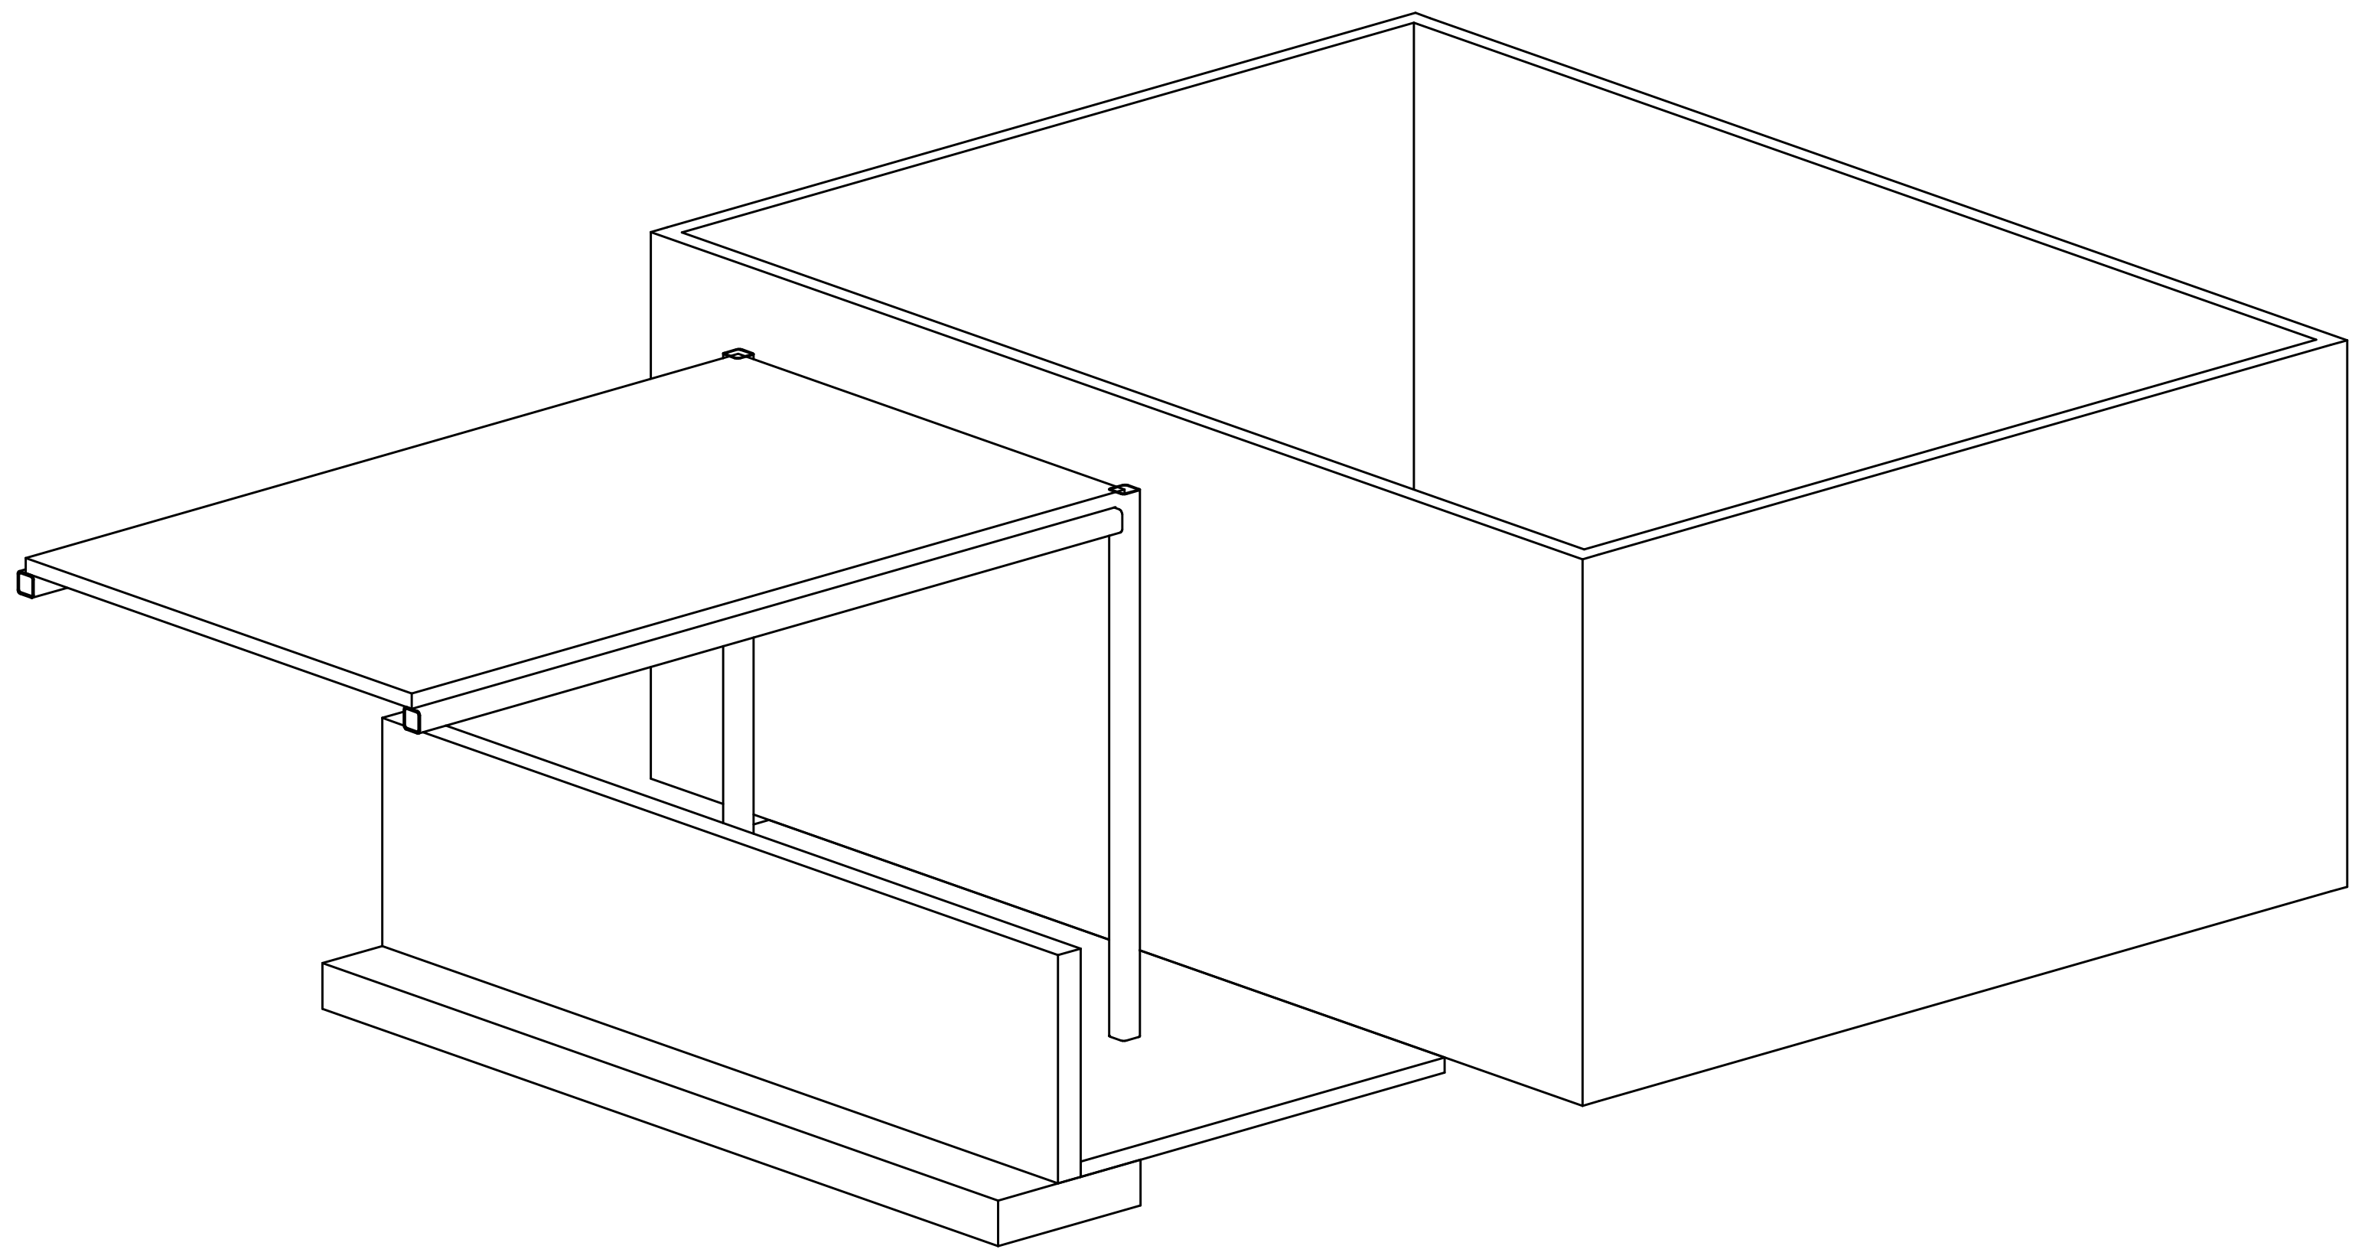

2 **ISOMETRIC**

1
S2.01

MM JOB #: ZZ.ZZZZ.S.XX
PRINCIPAL: Enter Principal's Name Here
EOR: Enter EOR's Name Here
PROJECT MANAGER: Enter PM's Name Here

DESIGNERS: Enter Designer's Name Here
LEAD REVIT TECH: Enter Lead Revit Tech's Name Here
DATE PRINTED: 5/22/2026 2:36:20 PM
FILE PATH: S:\Structural\ConnorK\ProjectFJ.rvt

MARTIN/MARTIN
CONSULTING ENGINEERS
12499 WEST COLFAX AVENUE, LAKEWOOD, COLORADO 80215
MAIN 303.431.6100 MARTINMARTIN.COM

PROGRESS PRINTS NOT
FOR CONSTRUCTION

EXTERNSHIP PROJECT

Enter Address Here

REVISIONS

NO.	ISSUE	DATE

PROJECT NO: ZZ.ZZZZ.S.XX
DATE: 05/21/26

© MARTIN/MARTIN 2025

SHEET TITLE:
PLAN VIEWS

SHEET NUMBER:
S2.00

Martin/Martin, Inc. considers that design data is only in its final form on plotted drawings with original signatures and professional certification being visibly present on the drawings. Data supplied via computer generated format does not contain this approval or certification. The receiver of electronically transmitted drawings is responsible for verifying the information contained within the electronic data against the recorded or approved documents.
The use of electronically transmitted drawings is considered to be at your own risk. Martin/Martin, Inc. assumes no responsibility for any claims or damages resulting from your use of this information. Electronic information is provided for the convenience of the recipient only. The recipient of this file agrees that the information may not be transferred to any other party.

MM JOB #: ZZ.ZZZZ.S.XX
PRINCIPAL: Enter Principal's Name Here
EOR: Enter EOR's Name Here
PROJECT MANAGER: Enter PM's Name Here

DESIGNERS: Enter Designer's Name Here
LEAD REVIT TECH: Enter Lead Revit Tech's Name Here
DATE PRINTED: 5/22/2026 2:36:20 PM
FILE PATH: S:\Structural\ConnorK\ProjectFJ.rvt

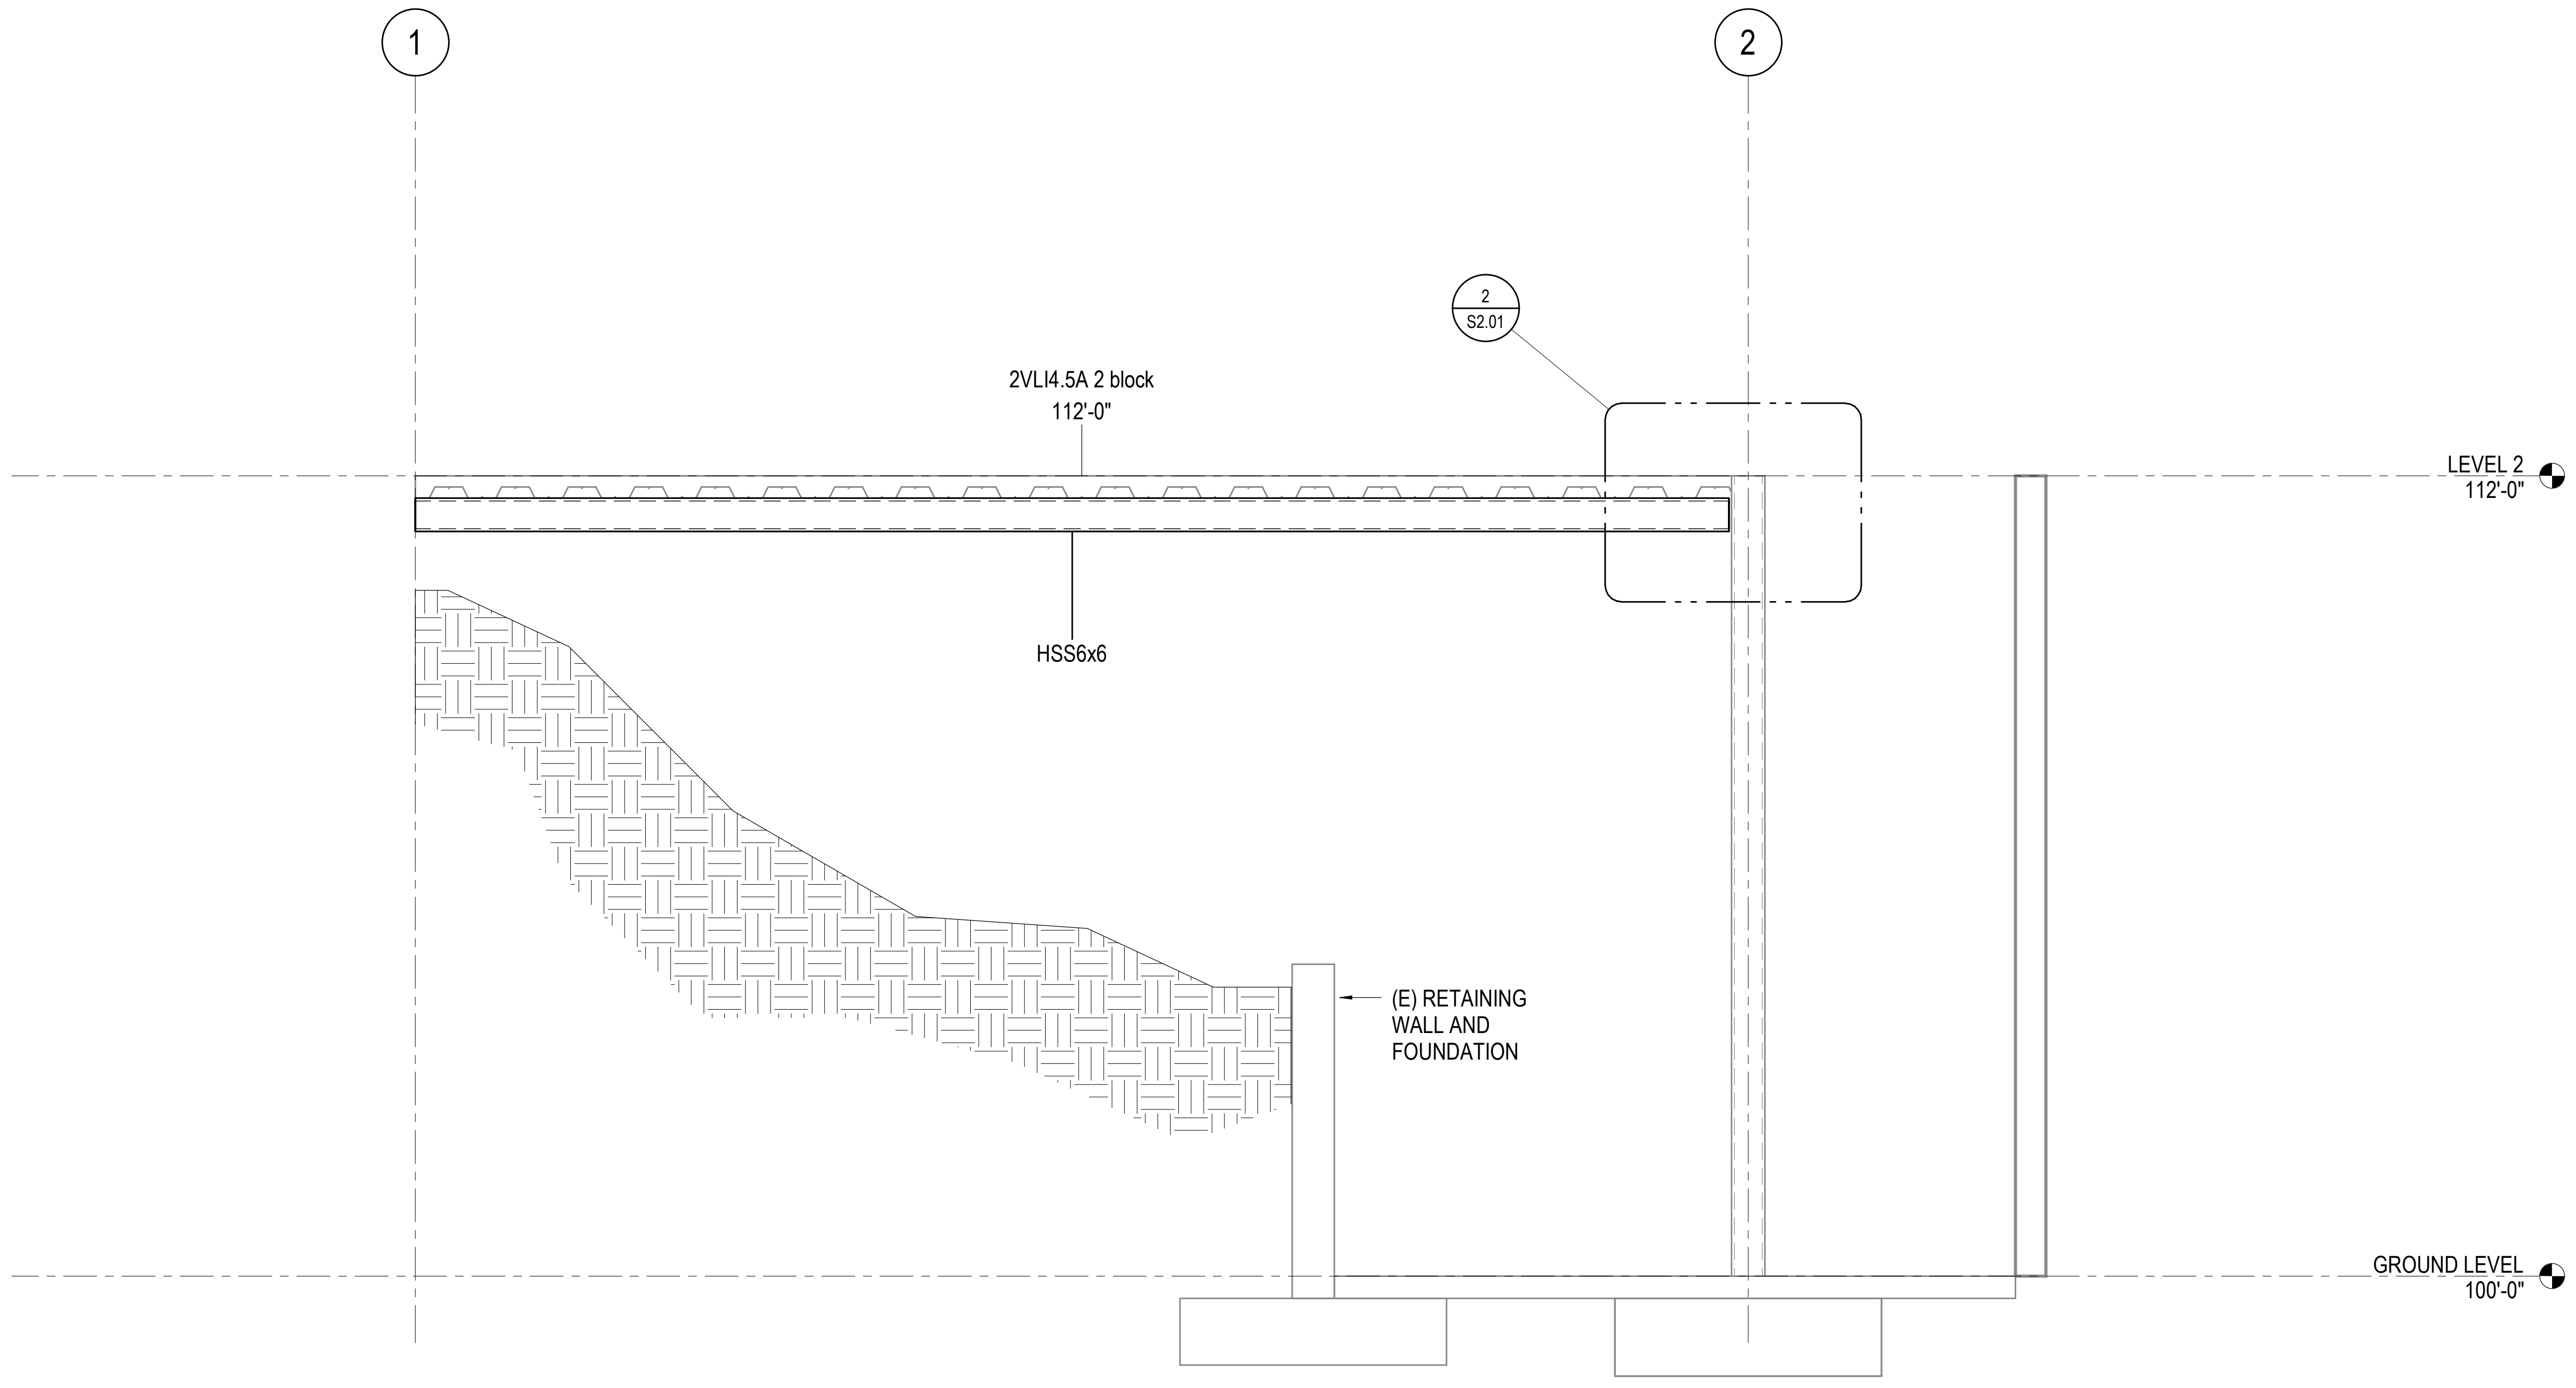

1 1/2" = 1'-0" ELEVATION 1 - b

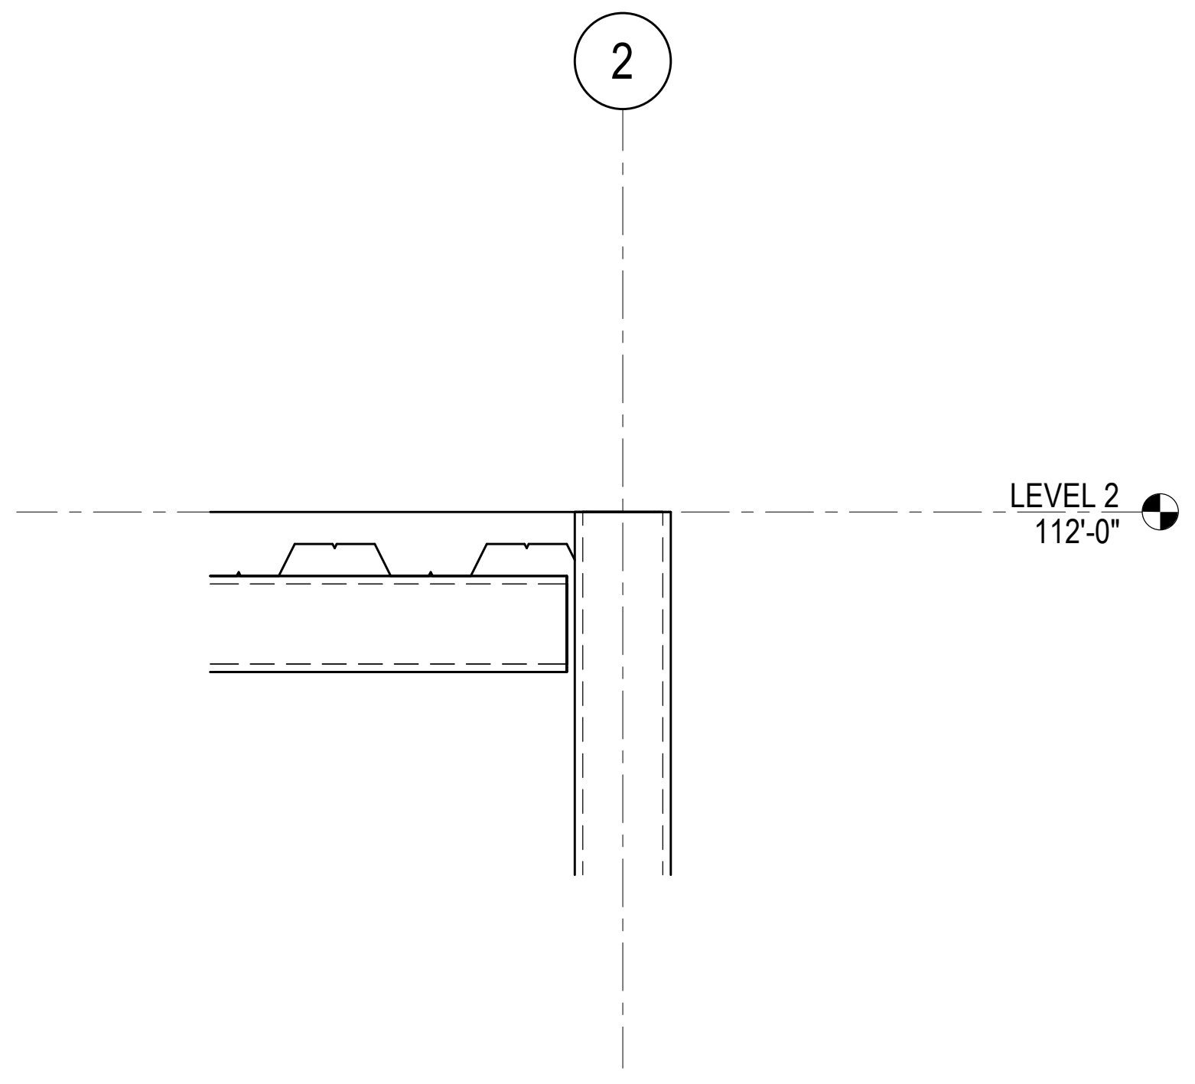

2 1" = 1'-0" BEAM CONNECTION

MARTIN/MARTIN
CONSULTING ENGINEERS
12499 WEST COLFAX AVENUE, LAKEWOOD, COLORADO 80215
MAIN 303.431.6100 MARTINMARTIN.COM

PROGRESS PRINTS NOT
FOR CONSTRUCTION

EXTERNSHIP PROJECT

Enter Address Here

REVISIONS

NO.	ISSUE	DATE

PROJECT NO: ZZ.ZZZZ.S.XX
DATE: 05/21/26

© MARTIN/MARTIN 2025

SHEET TITLE:
Unnamed

SHEET NUMBER:
S2.01

Martin/Martin, Inc. considers that design data is only in its final form on plotted drawings with original signatures and professional certification being visibly present on the drawings. Data supplied via computer generated format does not contain this approval or certification. The receiver of electronically transmitted drawings is responsible for verifying the information contained within the electronic data against the recorded or approved documents.
The use of electronically transmitted drawings is considered to be at your own risk. Martin/Martin, Inc. assumes no responsibility for any claims or damages resulting from your use of this information. Electronic information is provided for the convenience of the recipient only. The recipient of this file agrees that the information may not be transferred to any other party.